


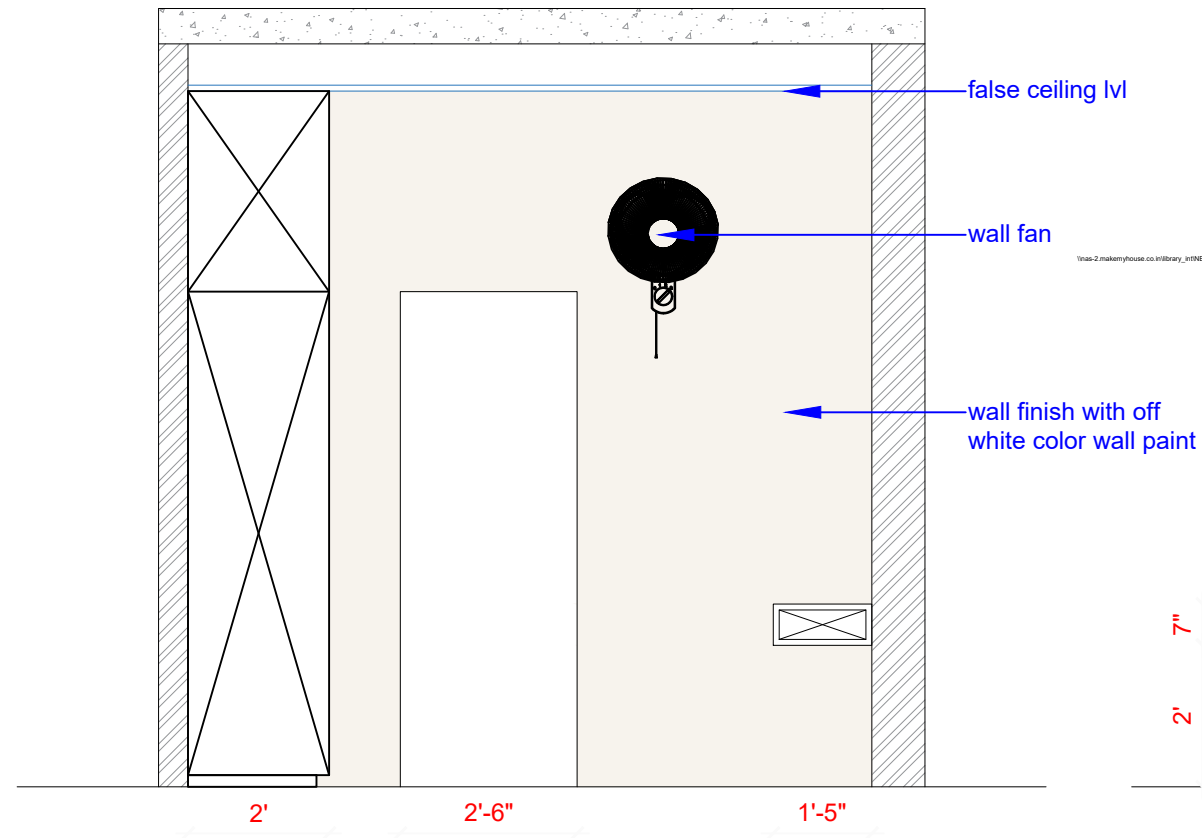


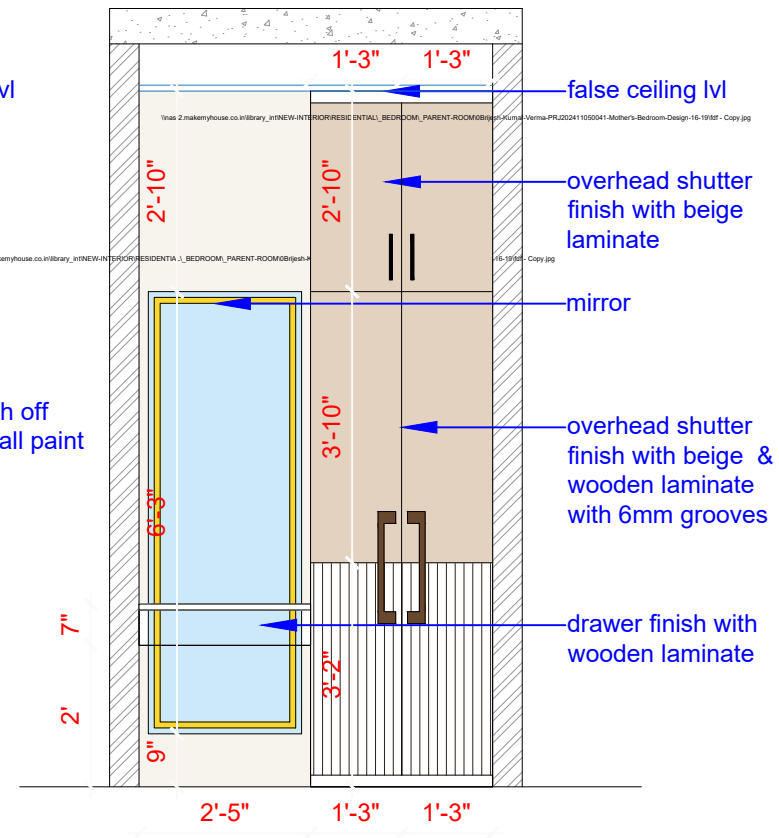


ELEVATION WALL A


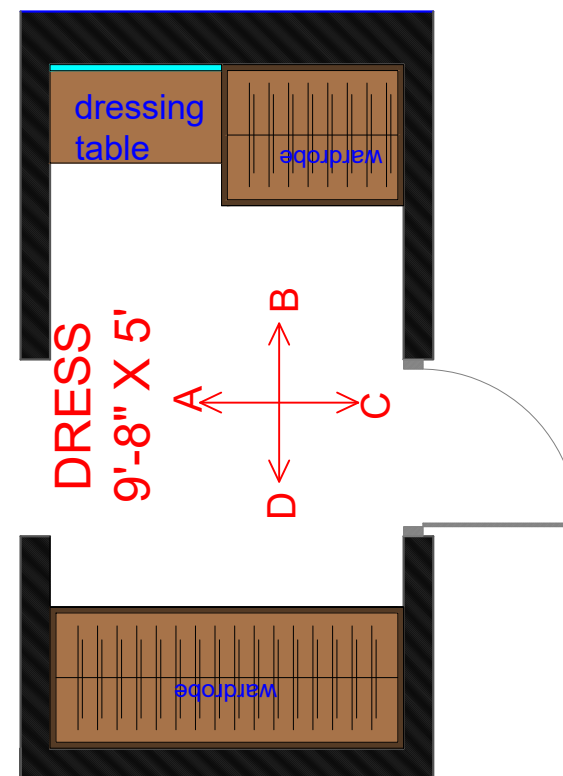


ELEVATION WALL B

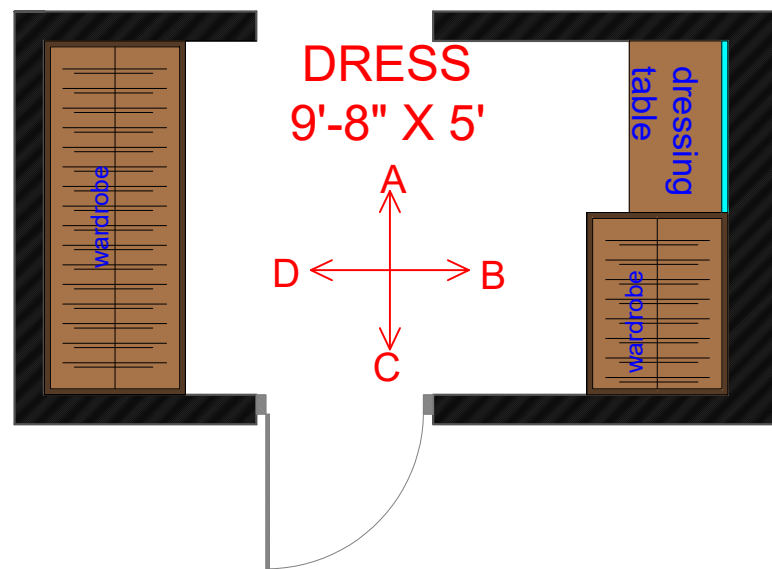


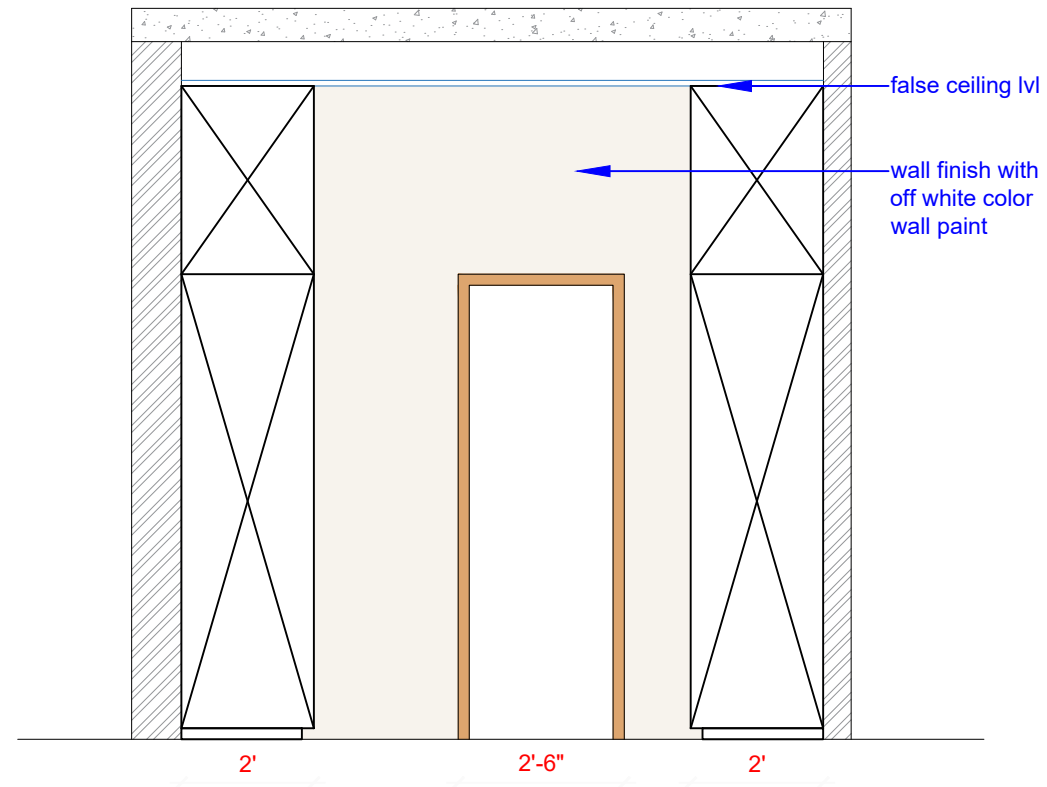


ELEVATION WALL C

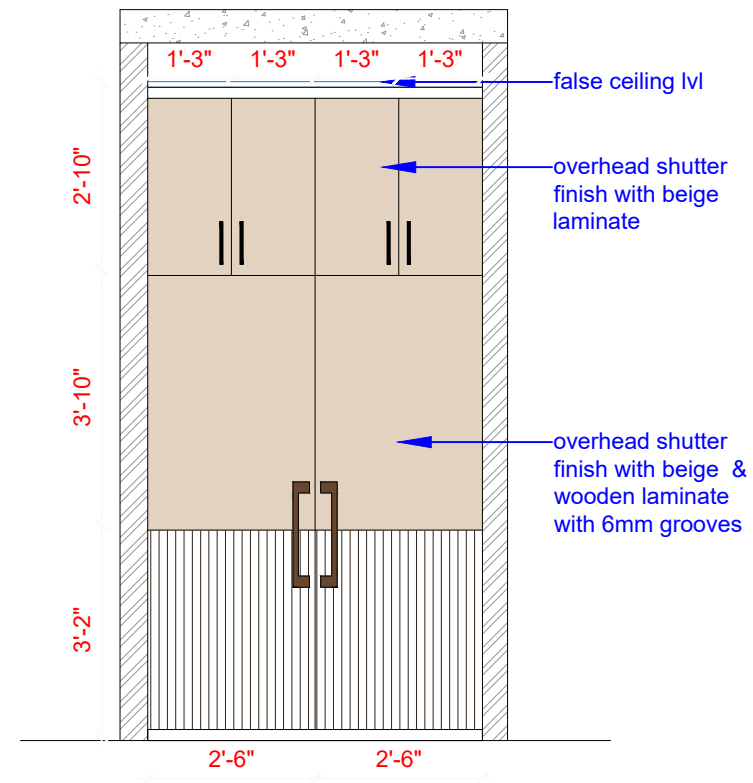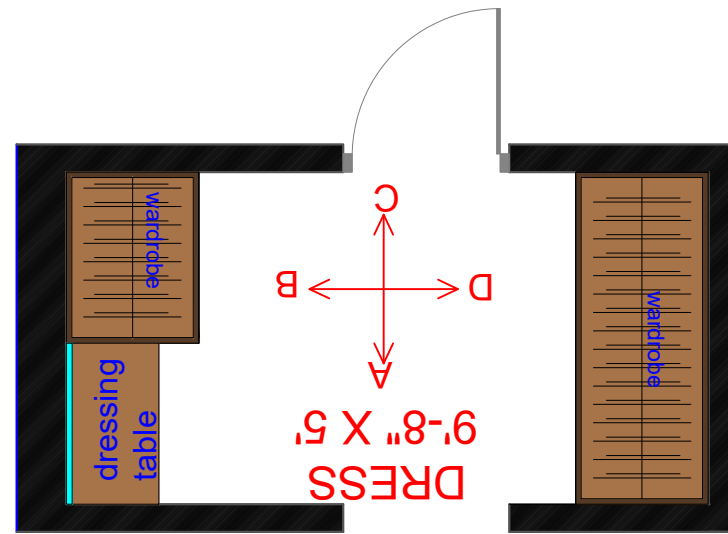


ELEVATION WALL D

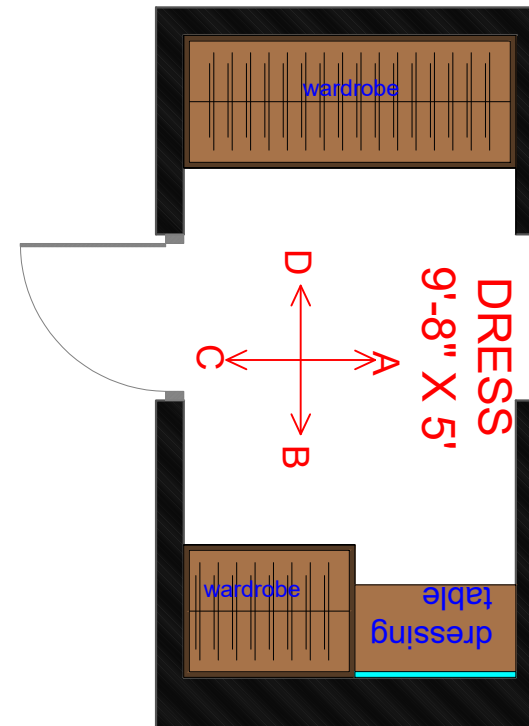

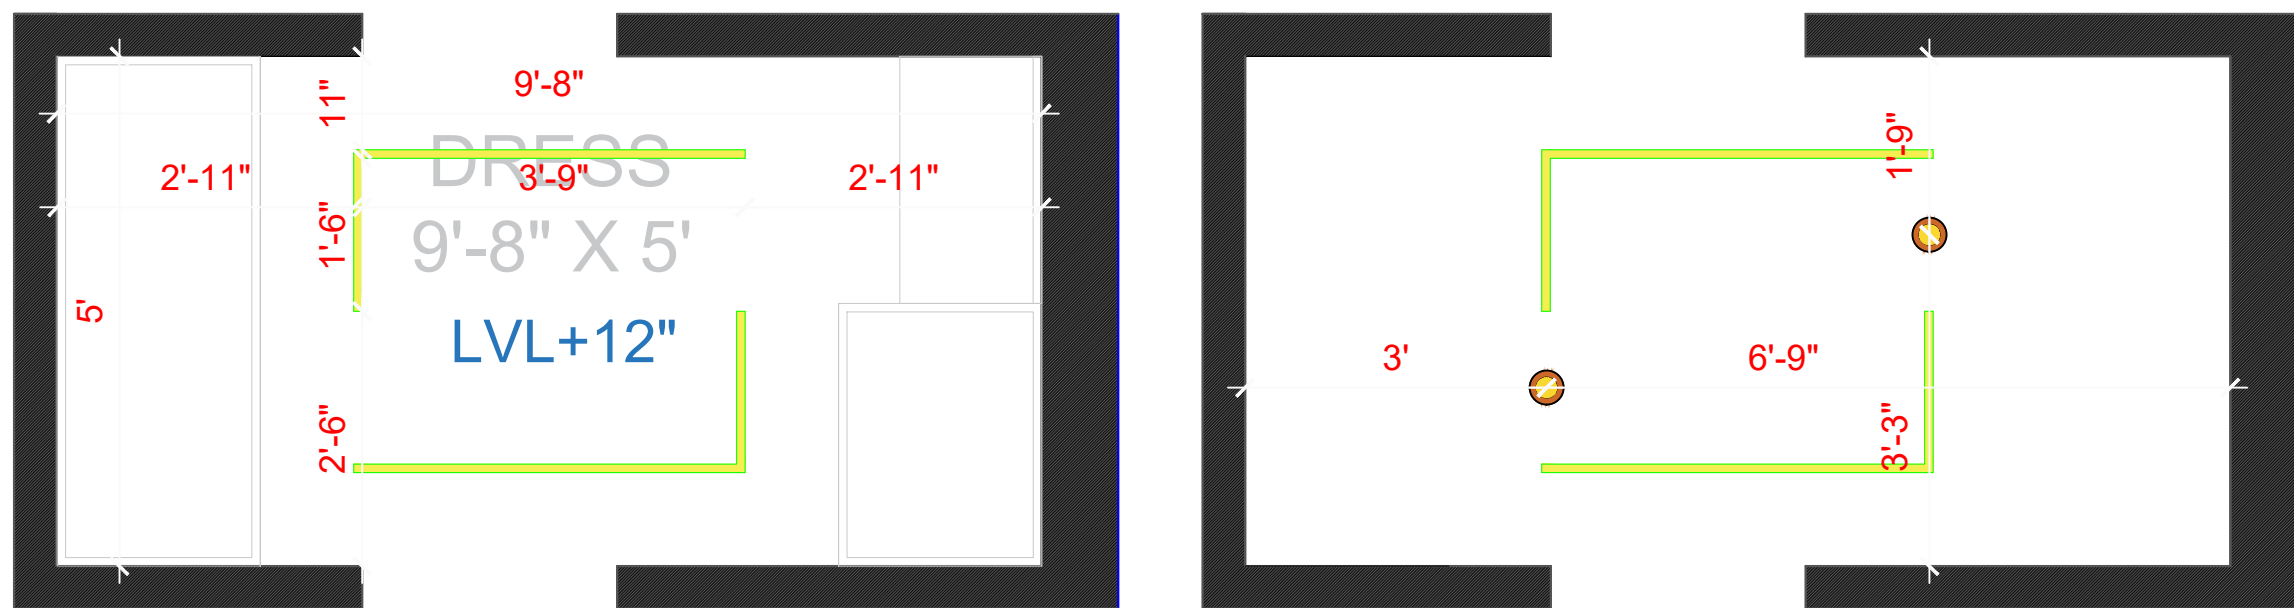

FALSE CEILING DETAIL & ELECTRICAL LAYOUT



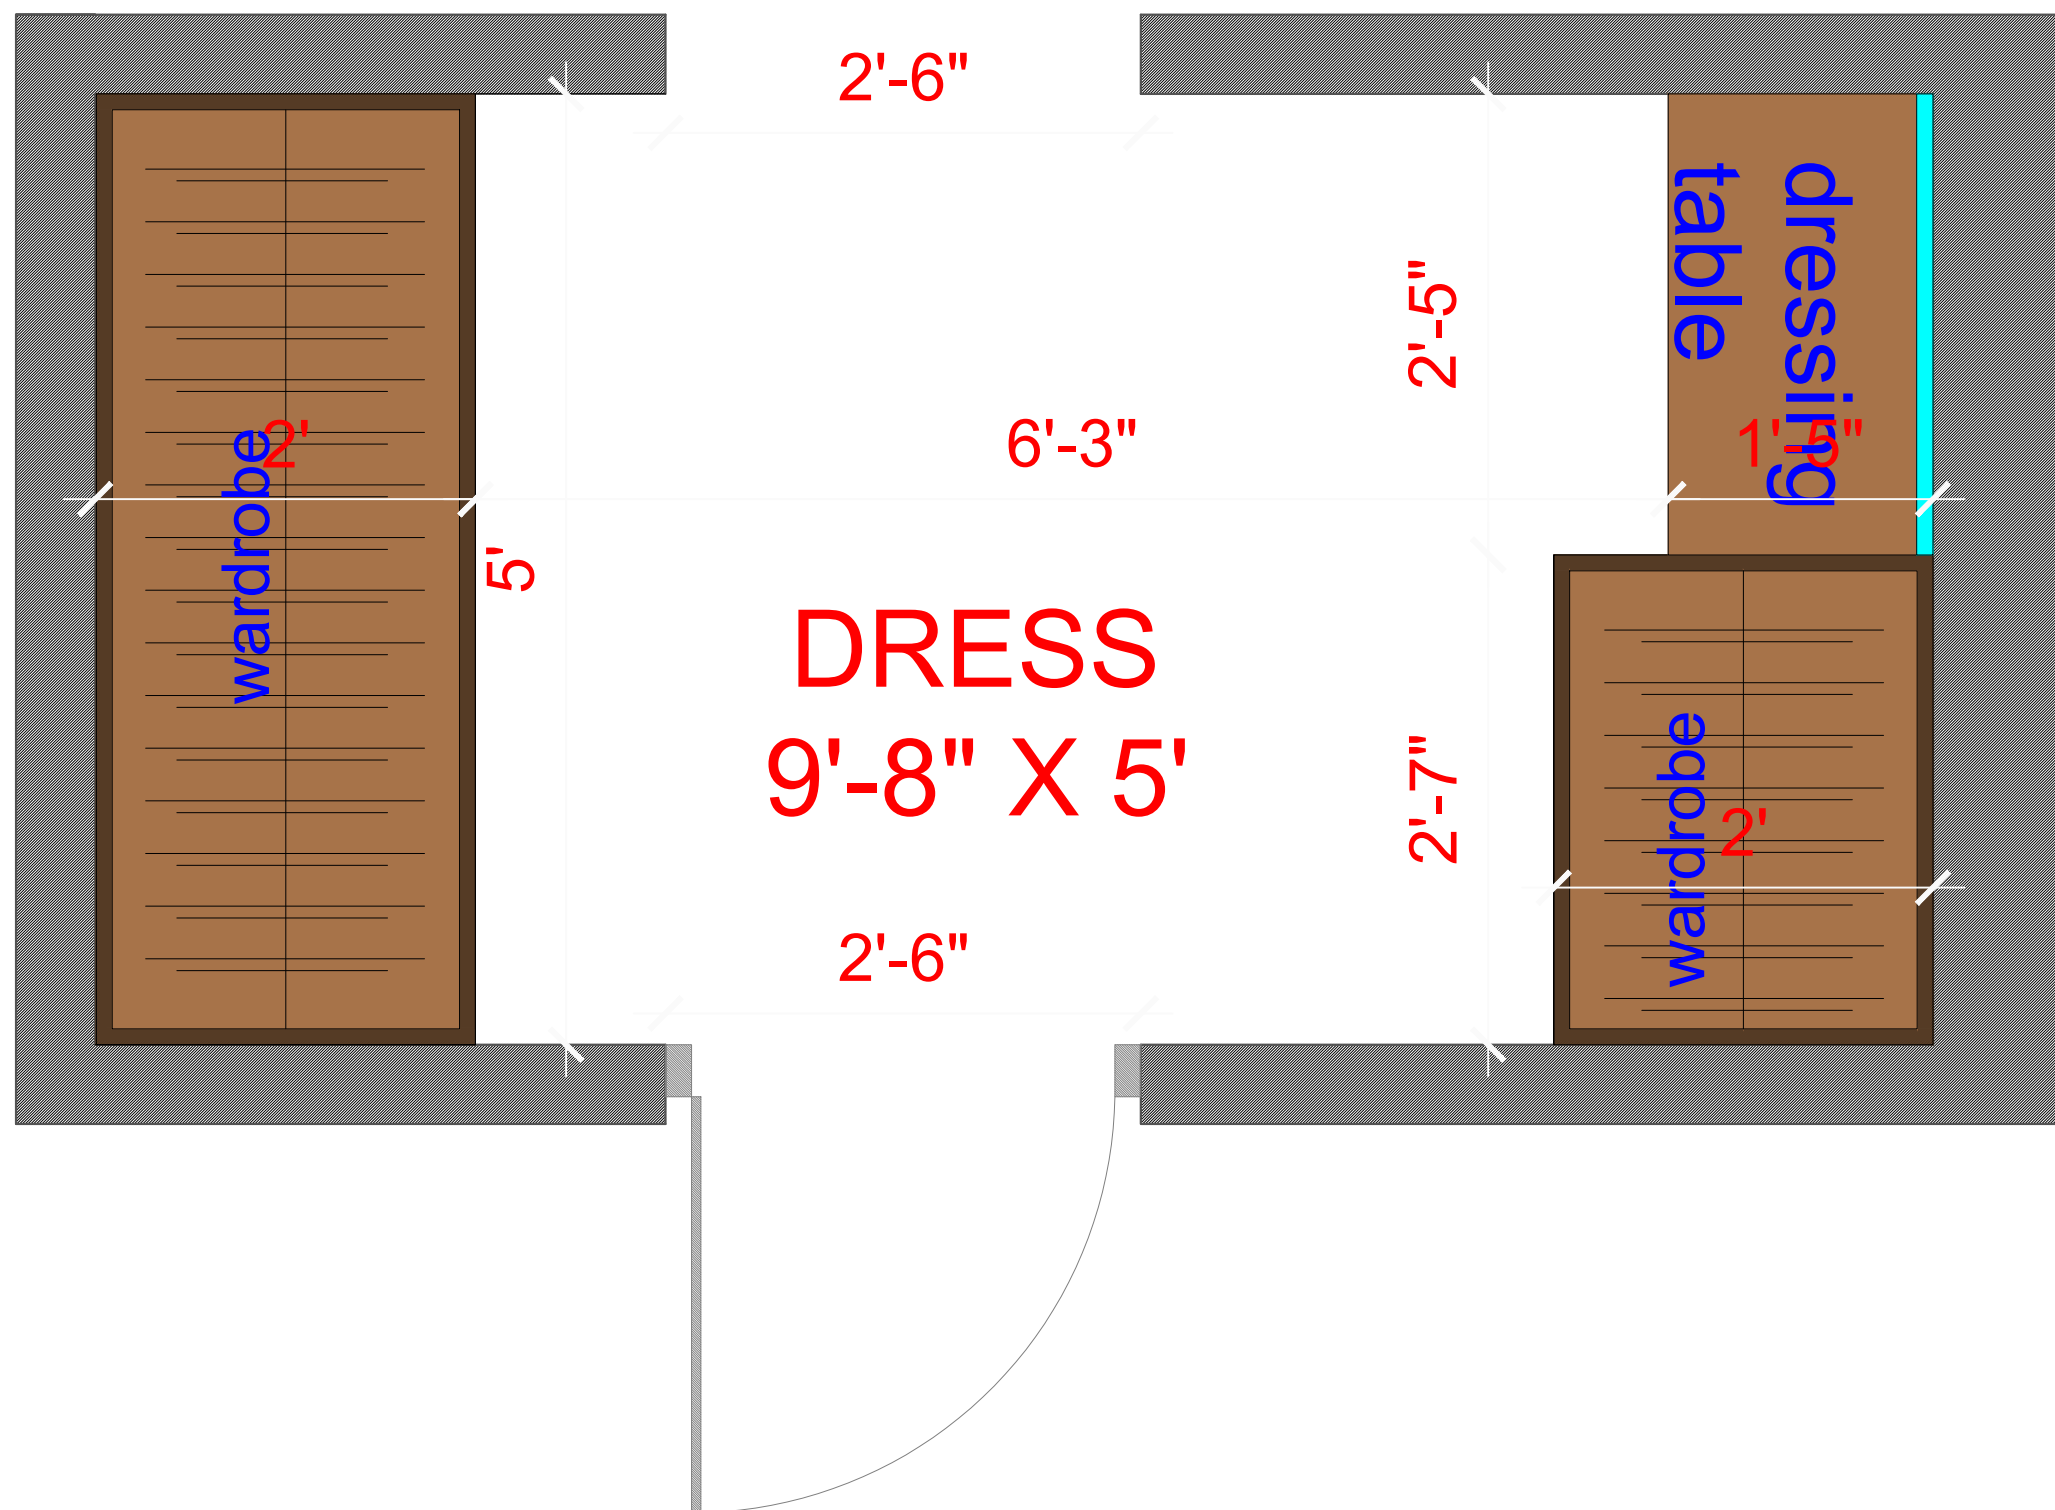

WORKING DRAWING